CONNECTING FLOOR
57'-9" X 20'-0"

COMM. DUCT

ELECTRICAL
PANEL ROOM
8'-8"X5'-11"

LADIES TOILET
19'-6"X7'-2"

TOILET 4'-0" X 5'-0"

TOILET 4'-0" X 5'-0"

TOILET 4'-0" X 5'-0"

TOILET 4'-0" X 5'-0"

TOILET 4'-0" X 5'-0"

GENTS TOILET
15'-6"X6'-5"

DN

71.73(+38'-0")

67.16(+33'-0")

UP

LIFT
7'2" X 4'0"

DRINKING WATER

LANDSCAPE

FUTURE EXPANSION

71.73(+38'-0")

UP

LANDSCAPE

71.73(+38'-0")

8'-0" WIDE
ENTRANCE

71.73(+38'-0")

DN

LANDSCAPE

DN

LANDSCAPE

LANDSCAPE

LANDSCAPE

UP

UP

ADMIN BLOCK ENTRANCE

70.51(+34'-0")

N NE E SE S SW W NW

GROUND FLOOR LVL (ADMINISTRATIVE BLOCK)

PROPOSED ADDITION OF 'ADMINISTRATIVE BLOCK' , TEACHING BLOCK
@ AIET CAMPUS MOODBIDRI

DATE: 18/12/2025


SCALE: 1:200

DRAWN BY : J.K

APPROVED BY:S.A

Arch Vista ARCHITECTURE

City Gate Commercial Complex,
4 Floor, Kadri, Mangalore - 575 002
Telephone : (0824 - 2214078)
e - mail : ar.sharun@gmail.com

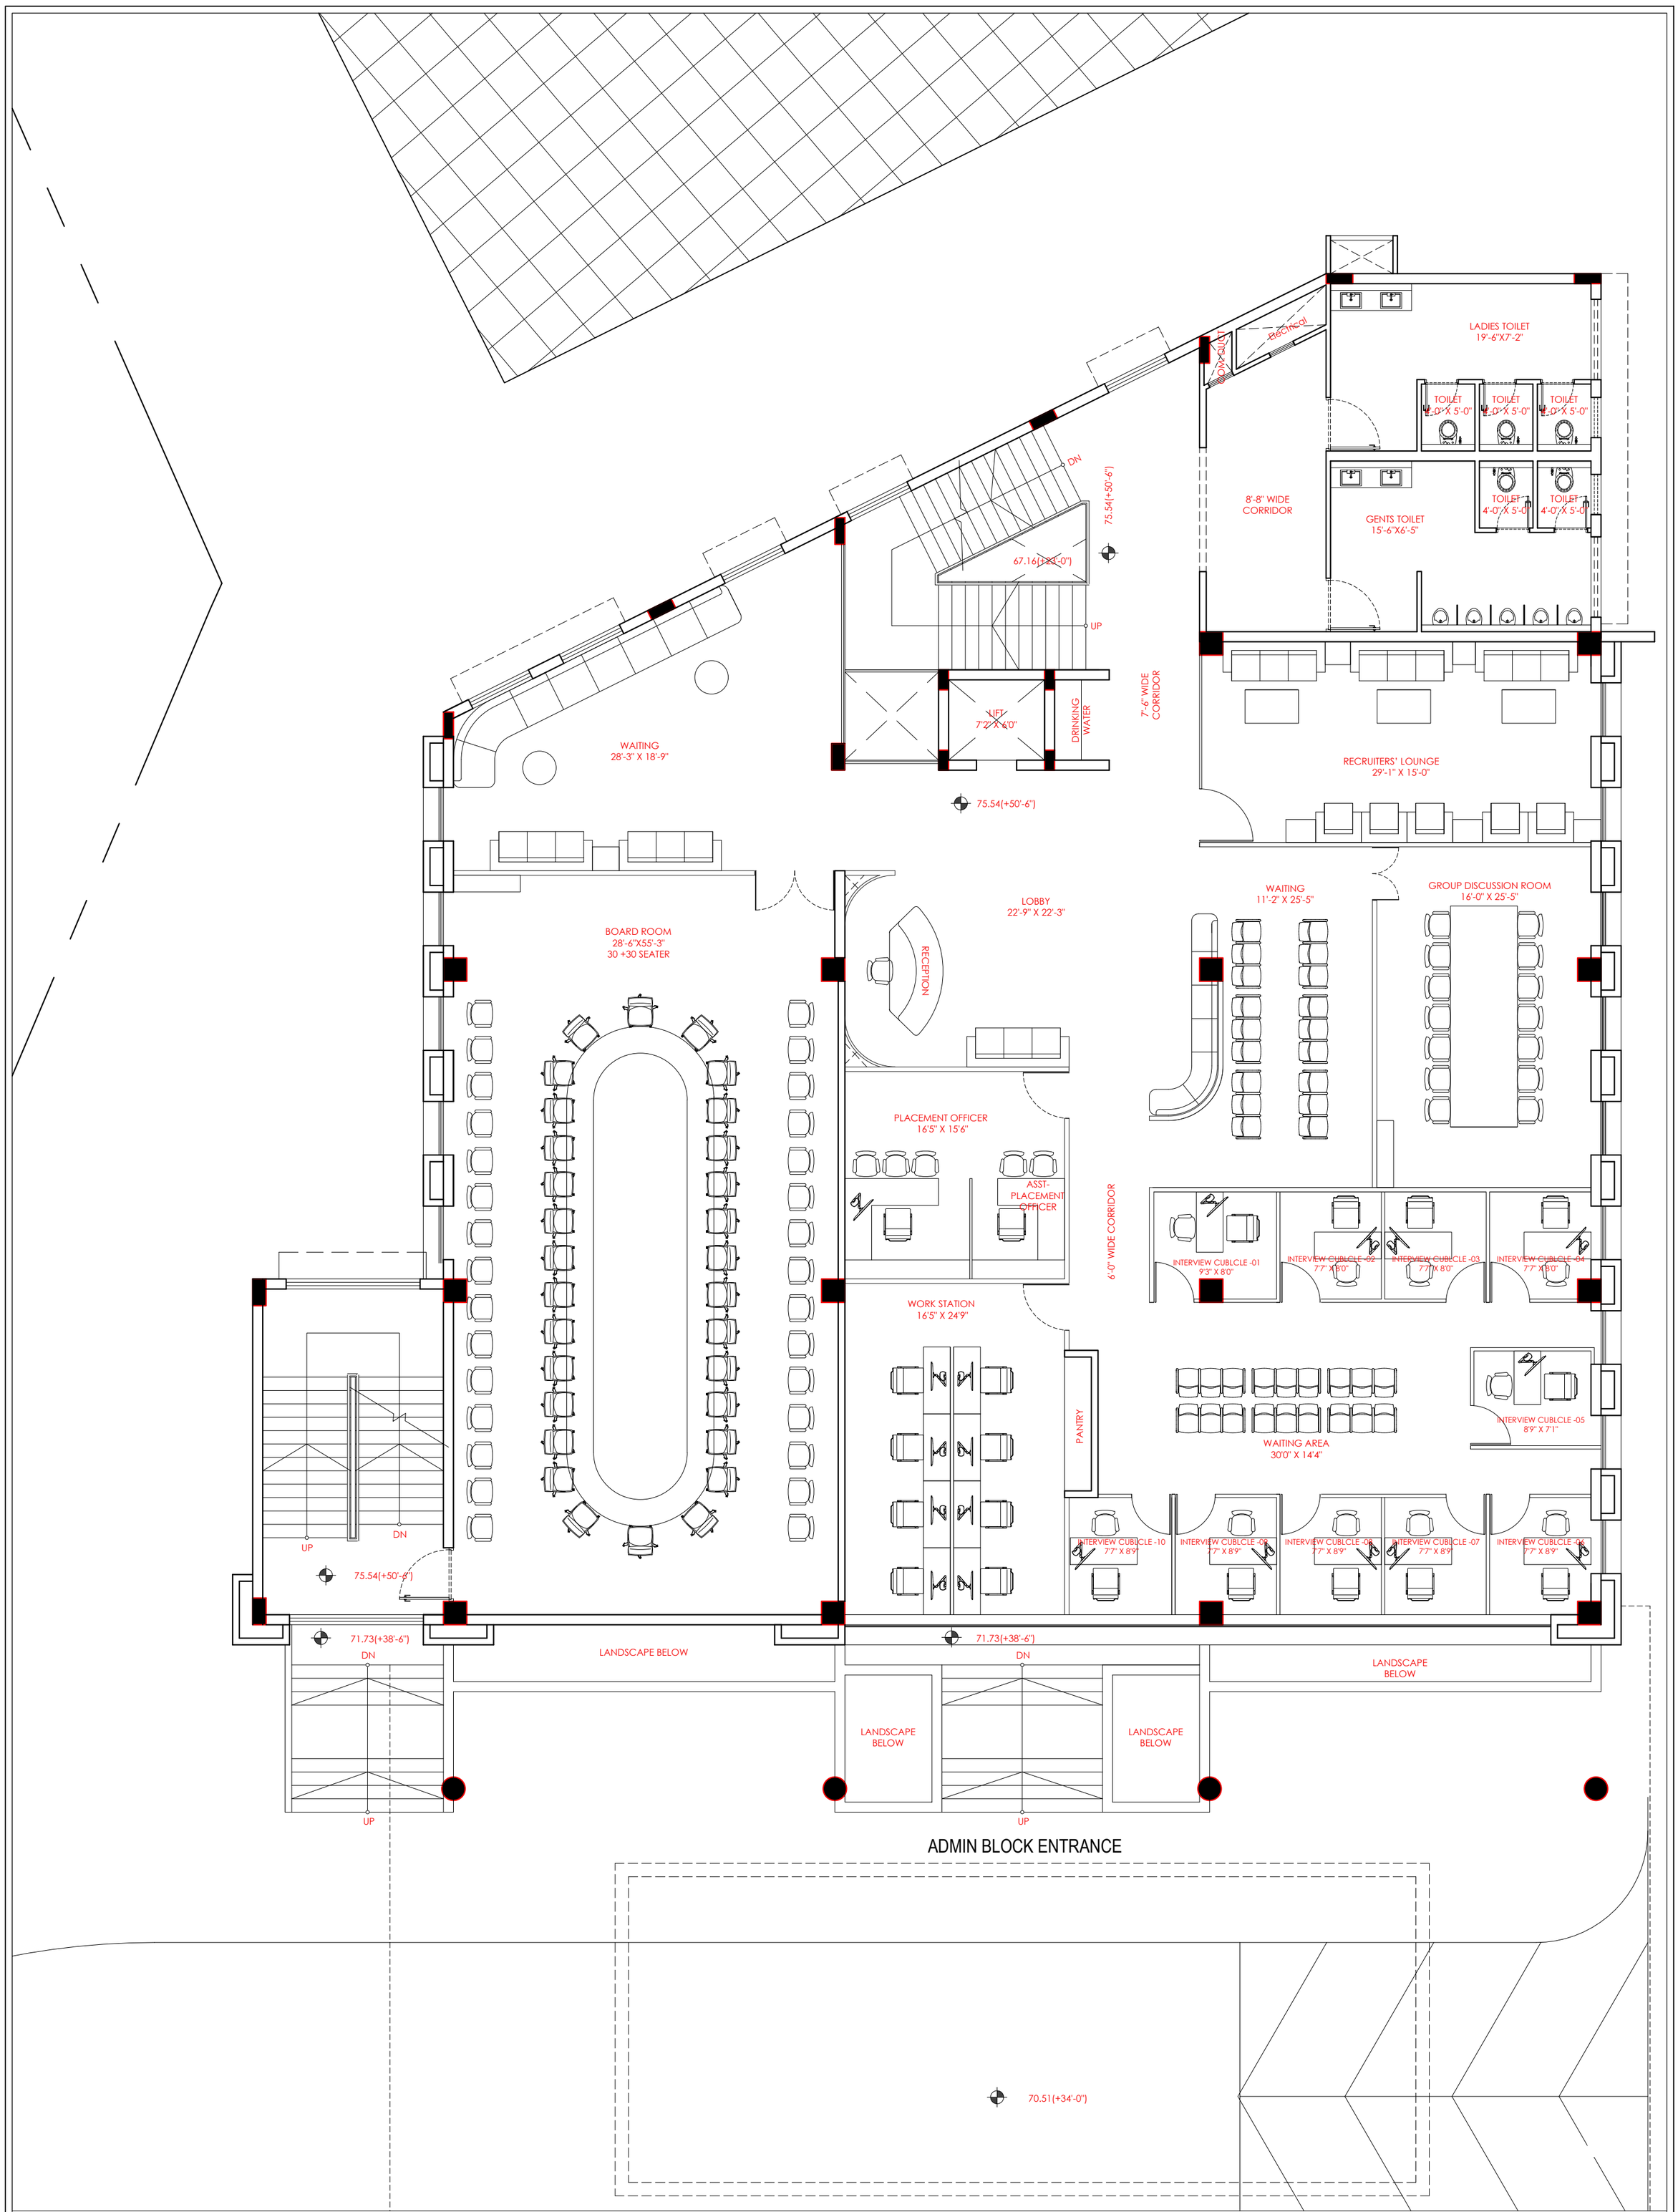


FIRST FLOOR LVL (ADMINISTRATIVE BLOCK)

PROPOSED ADDITION OF 'ADMINISTRATIVE BLOCK' , TEACHING BLOCK
@ AIET CAMPUS MOODBIDRI

DATE: 18/12/2025
SCALE: 1:200
DRAWN BY : J.K
APPROVED BY:S.A

Arch Vista ARCHITECTURE
City Gate Commercial Complex,
4 Floor, Kadri, Mangalore - 575 002
Telephone : (0824 - 2214078)
e - mail : ar.sharun@gmail.com

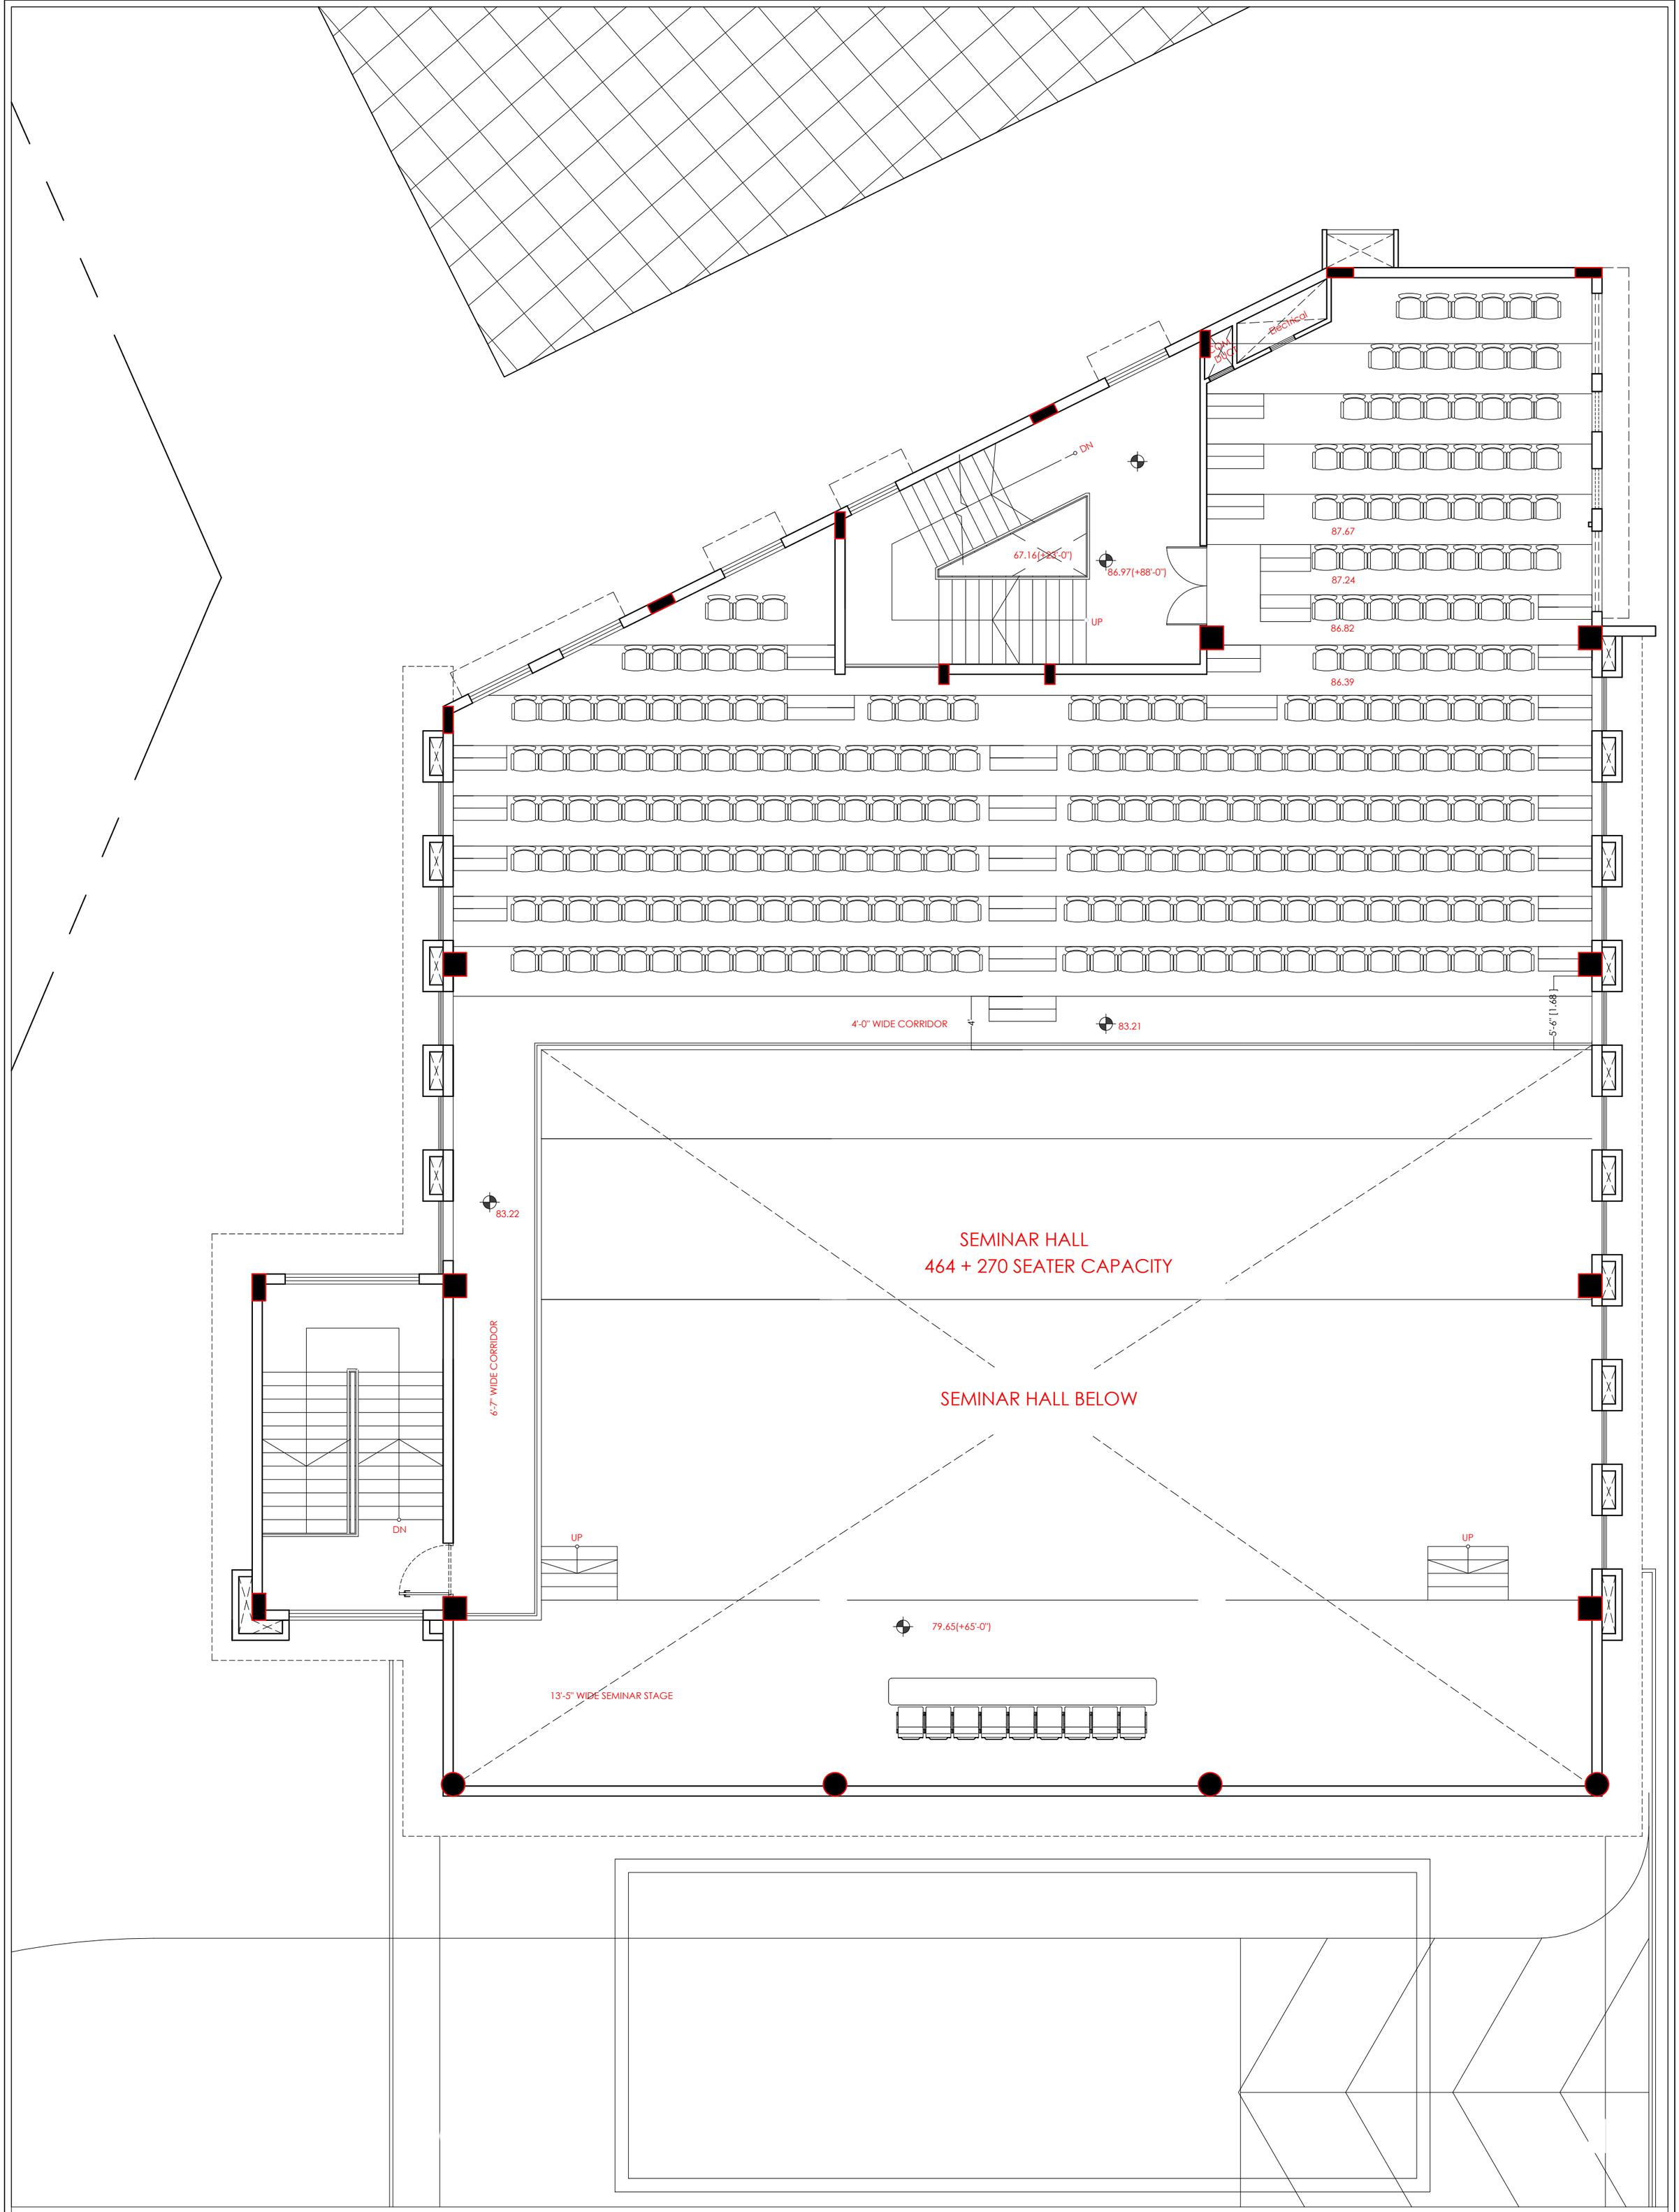

2ND FLOOR

SEMINAR HALL UPPER GALLERY LVL PLAN

PROPOSED ADDITION OF 'ADMINISTRATIVE BLOCK' , TEACHING BLOCK
@ AIET CAMPUS MOODBIDRI


DATE: 18/12/2025

SCALE: 1:200

DRAWN BY : J.K

APPROVED BY:S.A

Arch Vista ARCHITECTURE
City Gate Commercial Complex,
4 Floor, Kadri, Mangalore - 575 002
Telephone : (0824 - 2214078)
e - mail : ar.sharun@gmail.com

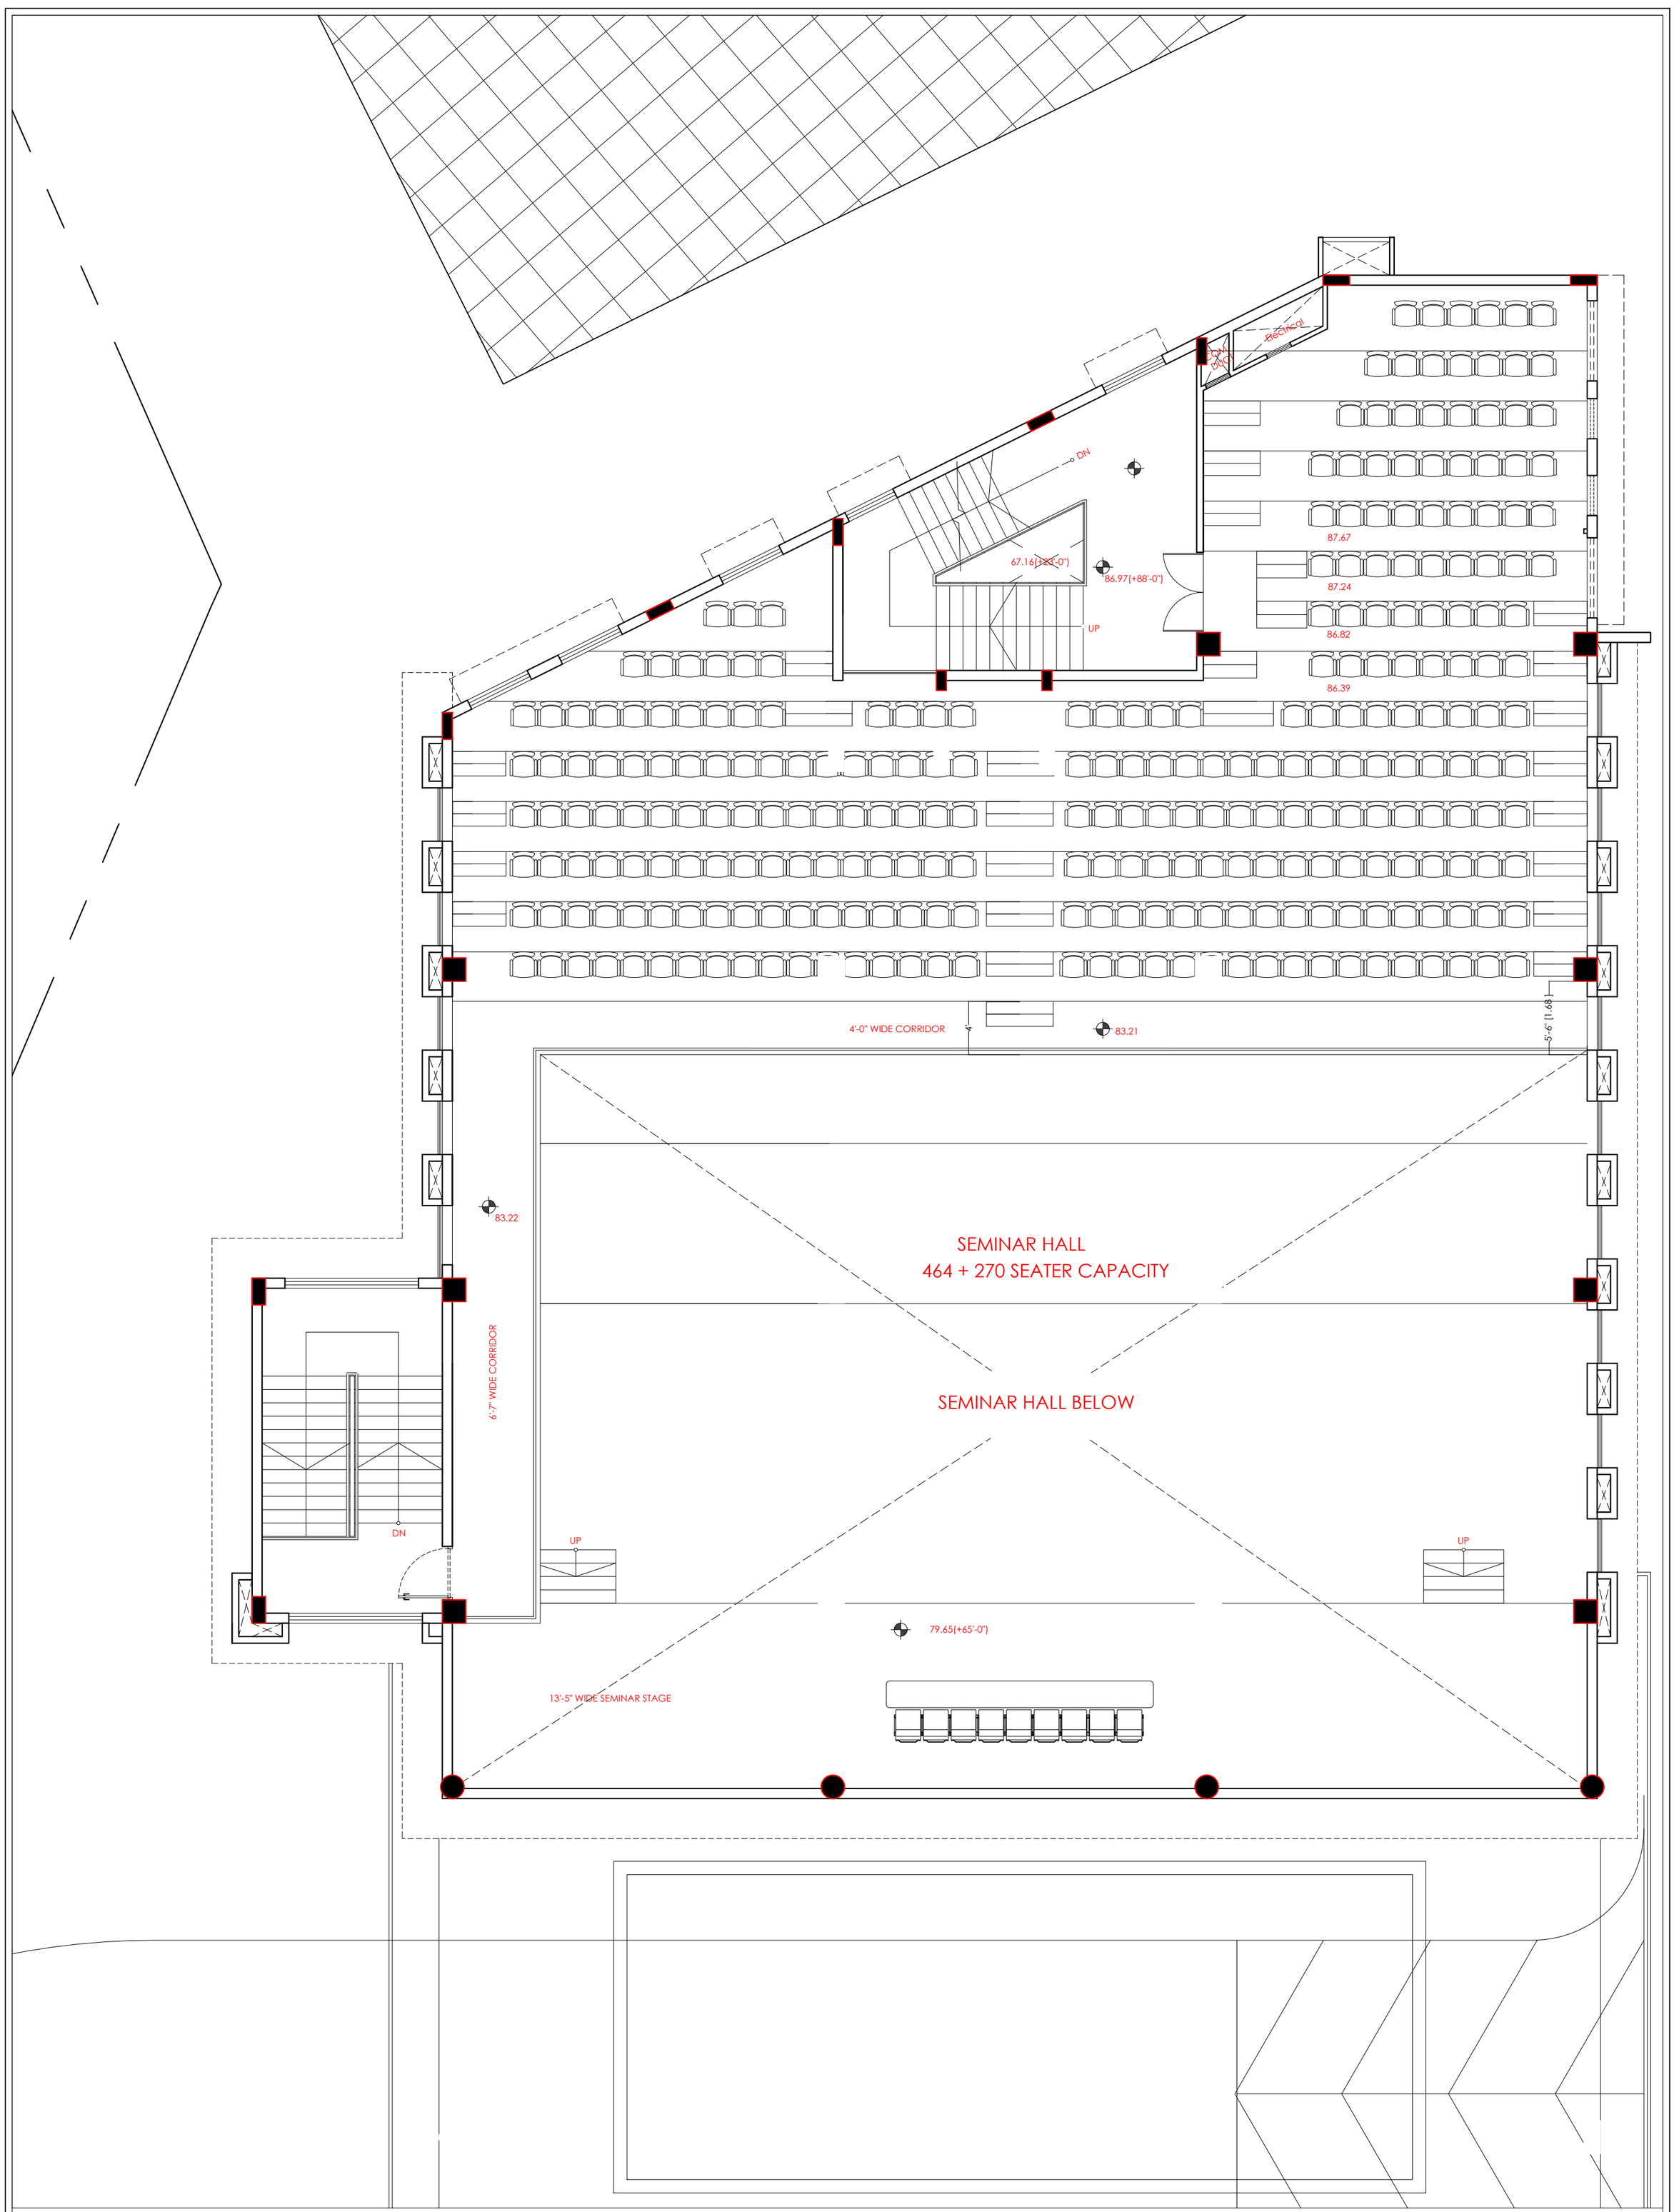

2ND FLOOR

SEMINAR HALL UPPER GALLERY LVL PLAN

PROPOSED ADDITION OF 'ADMINISTRATIVE BLOCK' , TEACHING BLOCK @ AIET CAMPUS MOODBIDRI

DATE: 18/12/2025

SCALE: 1:200

DRAWN BY : J.K

APPROVED BY:S.A

Arch Vista ARCHITECTURE

City Gate Commercial Complex,
4 Floor, Kadri, Mangalore - 575 002
Telephone : (0824 - 2214078)
e - mail : ar.sharun@gmail.com