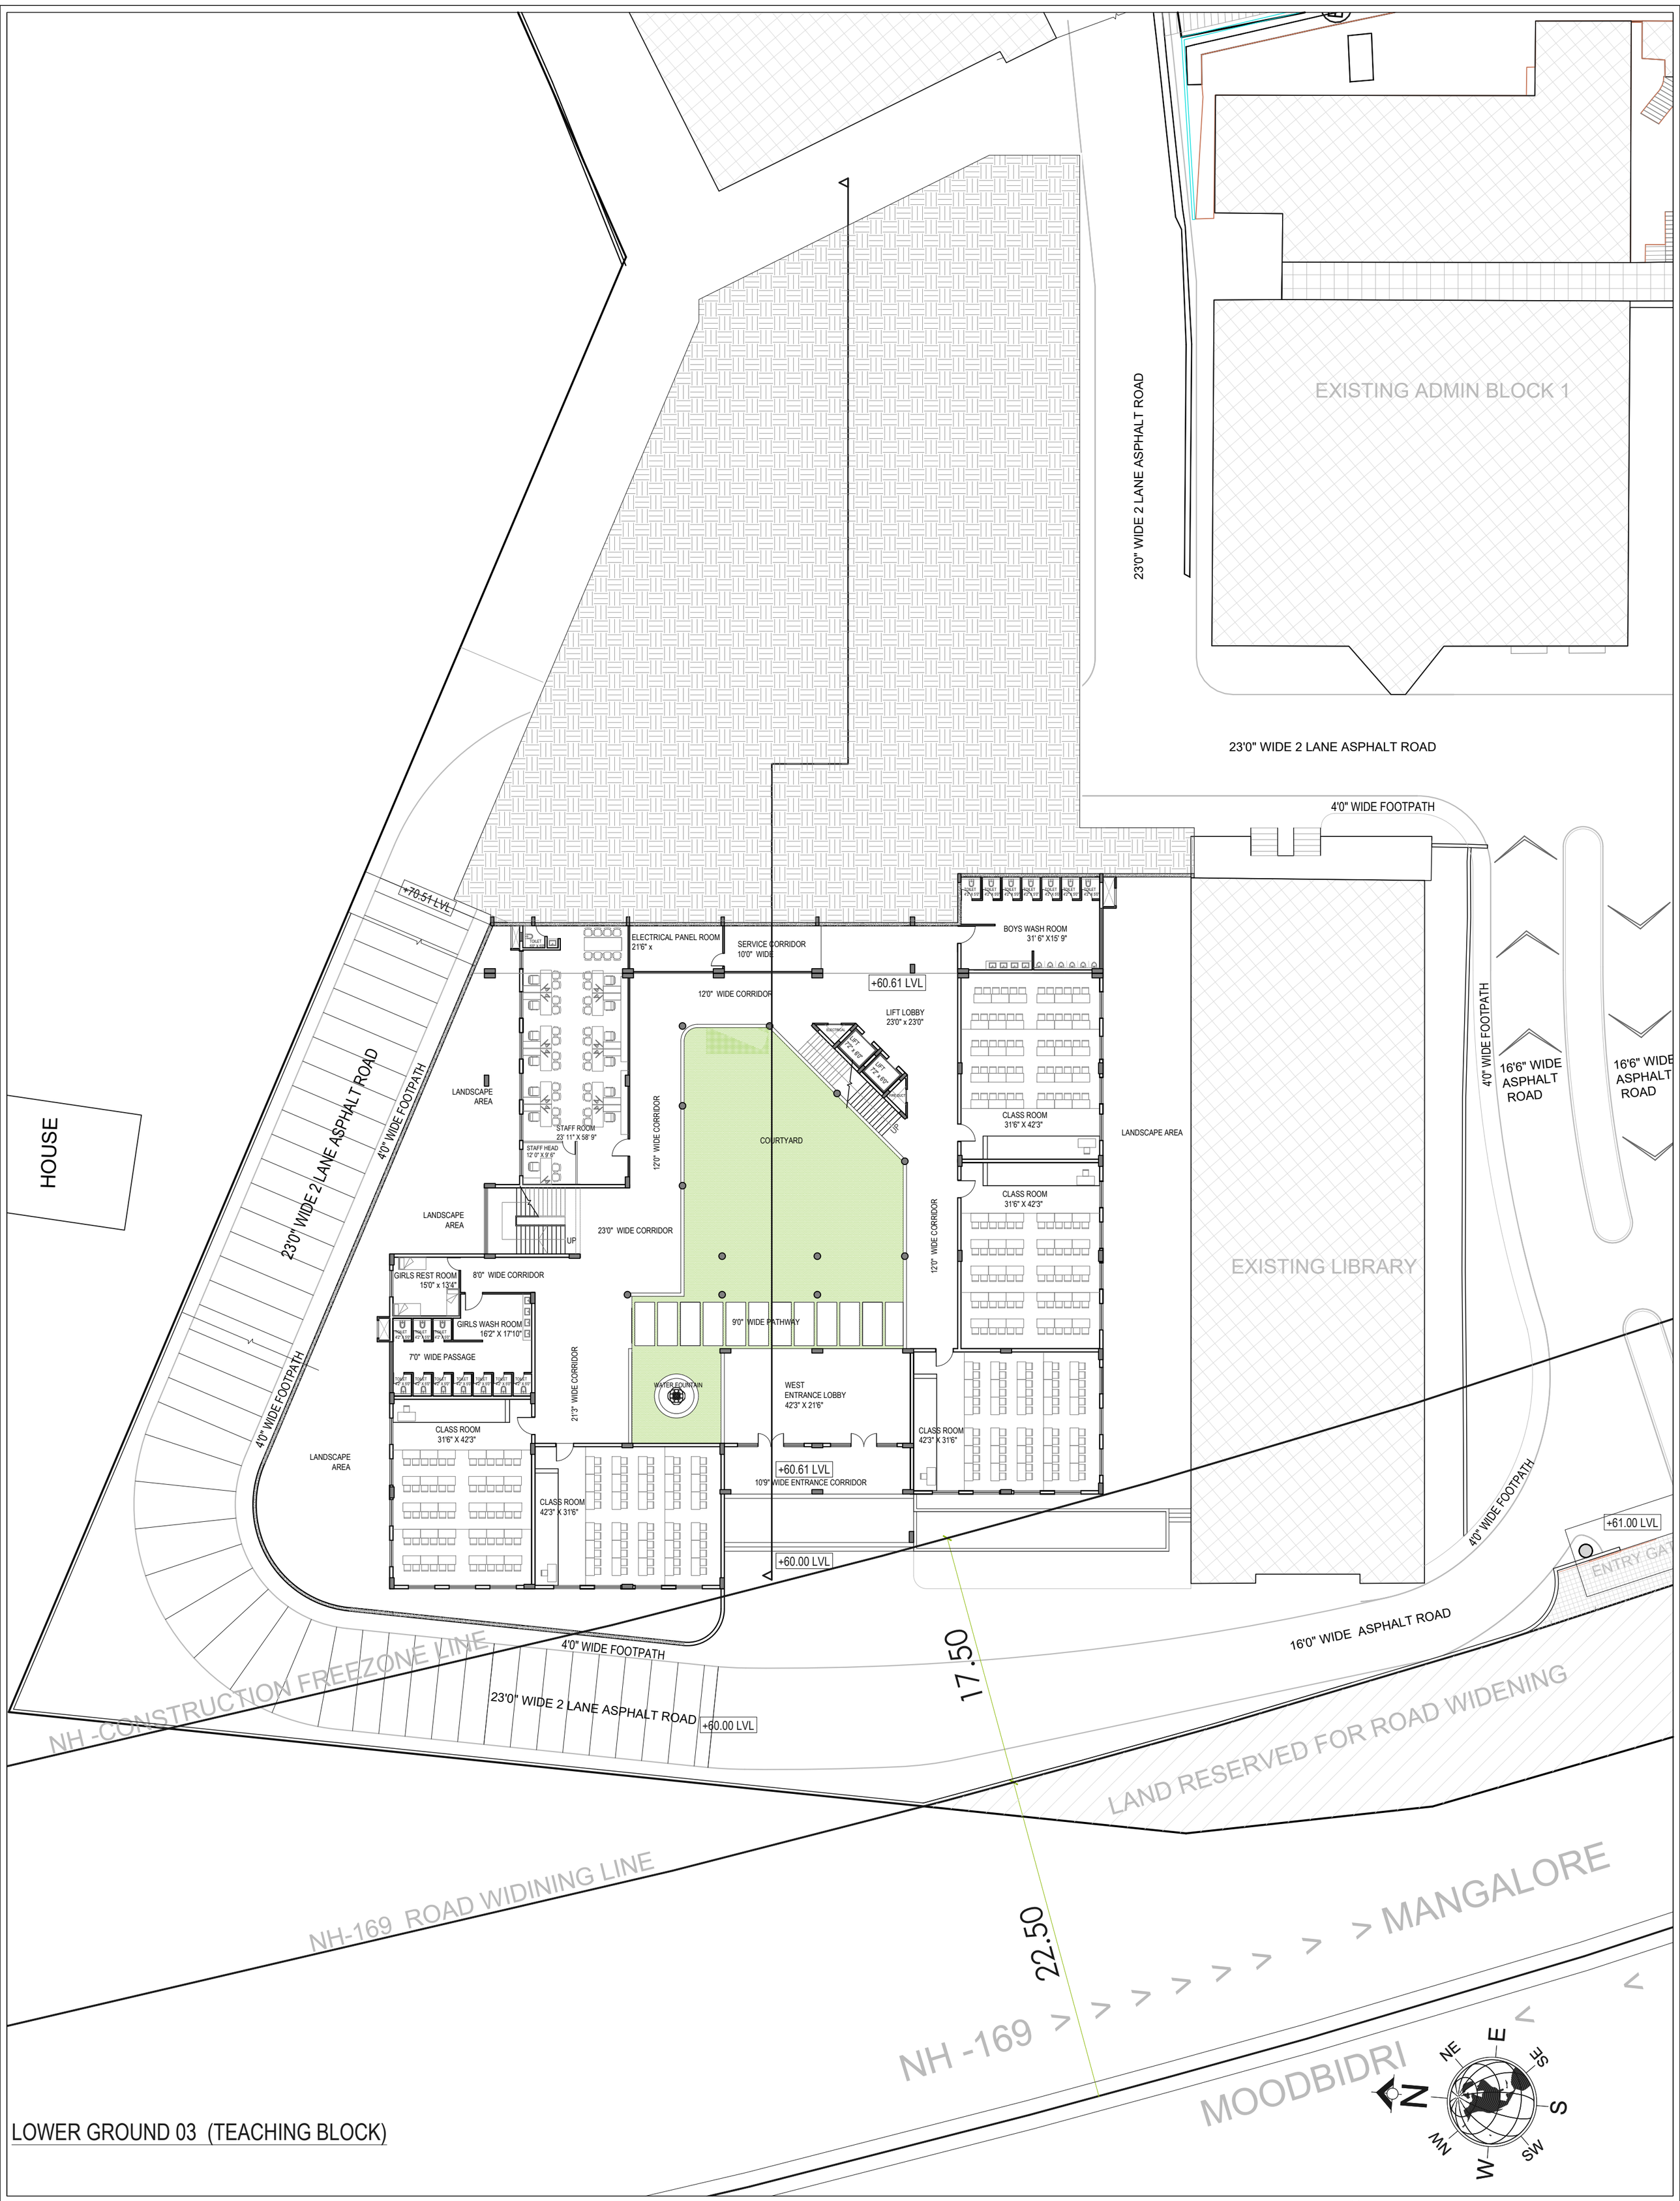


LOWER GROUND 03 (TEACHING BLOCK)

PROPOSED ADDITION OF 'ADMINISTRATIVE BLOCK' , TEACHING BLOCK @ AIET CAMPUS MOODBIDRI

SHEET NO- 01 OF 08

2025-INS -58-CS-IP-DRA-ZO-001 V3 R2

DATE: 17/03/2025


SCALE: 1:200

DRAWN BY : J.K

APPROVED BY:S.A

Arch Vista ARCHITECTURE

City Gate Commercial Complex,
4 Floor, Kadri, Mangalore - 575 002
Telephone : (0824 - 2214078)
e - mail : ar.sharun@gmail.com

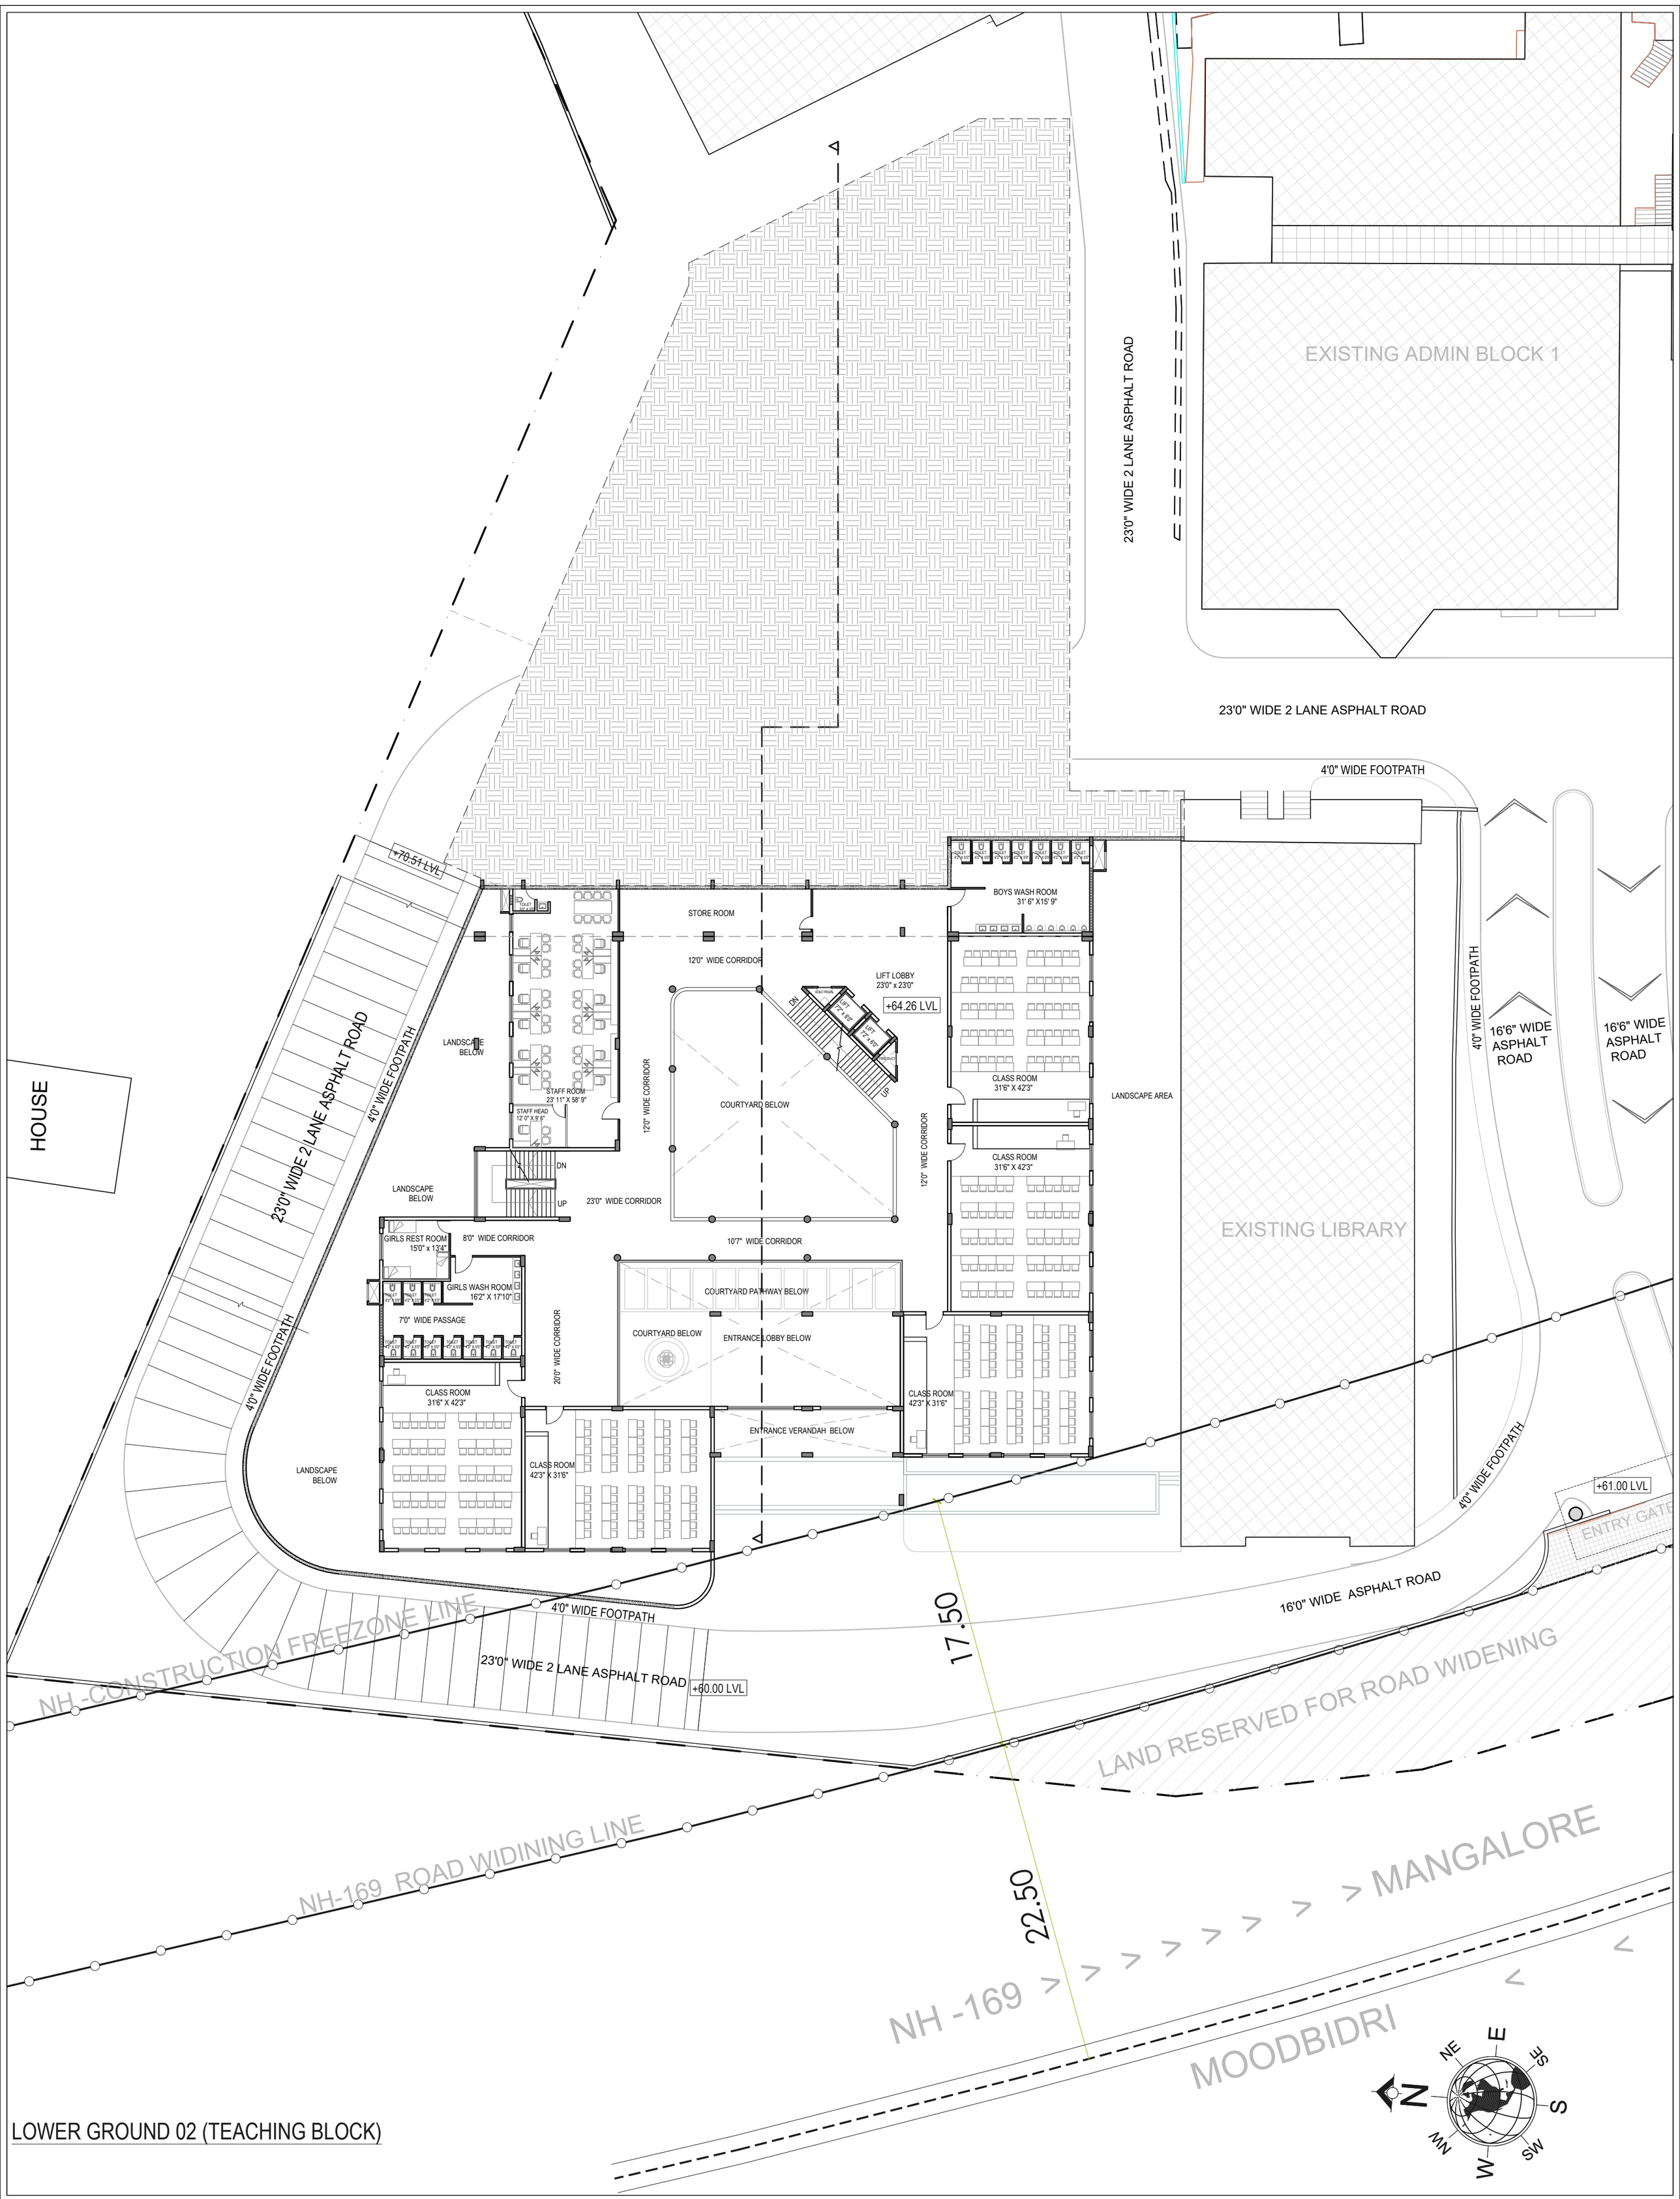

LOWER GROUND 02 (TEACHING BLOCK)

PROPOSED ADDITION OF 'ADMINISTRATIVE BLOCK' , TEACHING BLOCK
@ AIET CAMPUS MOODBIDRI

SHEET NO- 02 OF 08

2025-INS -58-CS-IP-DRA-ZO-001 V3 R2

DATE: 17/03/2025


SCALE: 1:200

DRAWN BY : J.K

APPROVED BY:S.A

Arch Vista ARCHITECTURE

City Gate Commercial Complex,
4 Floor, Kadri, Mangalore - 575 002
Telephone : (0824 - 2214078)
e - mail : ar.sharun@gmail.com

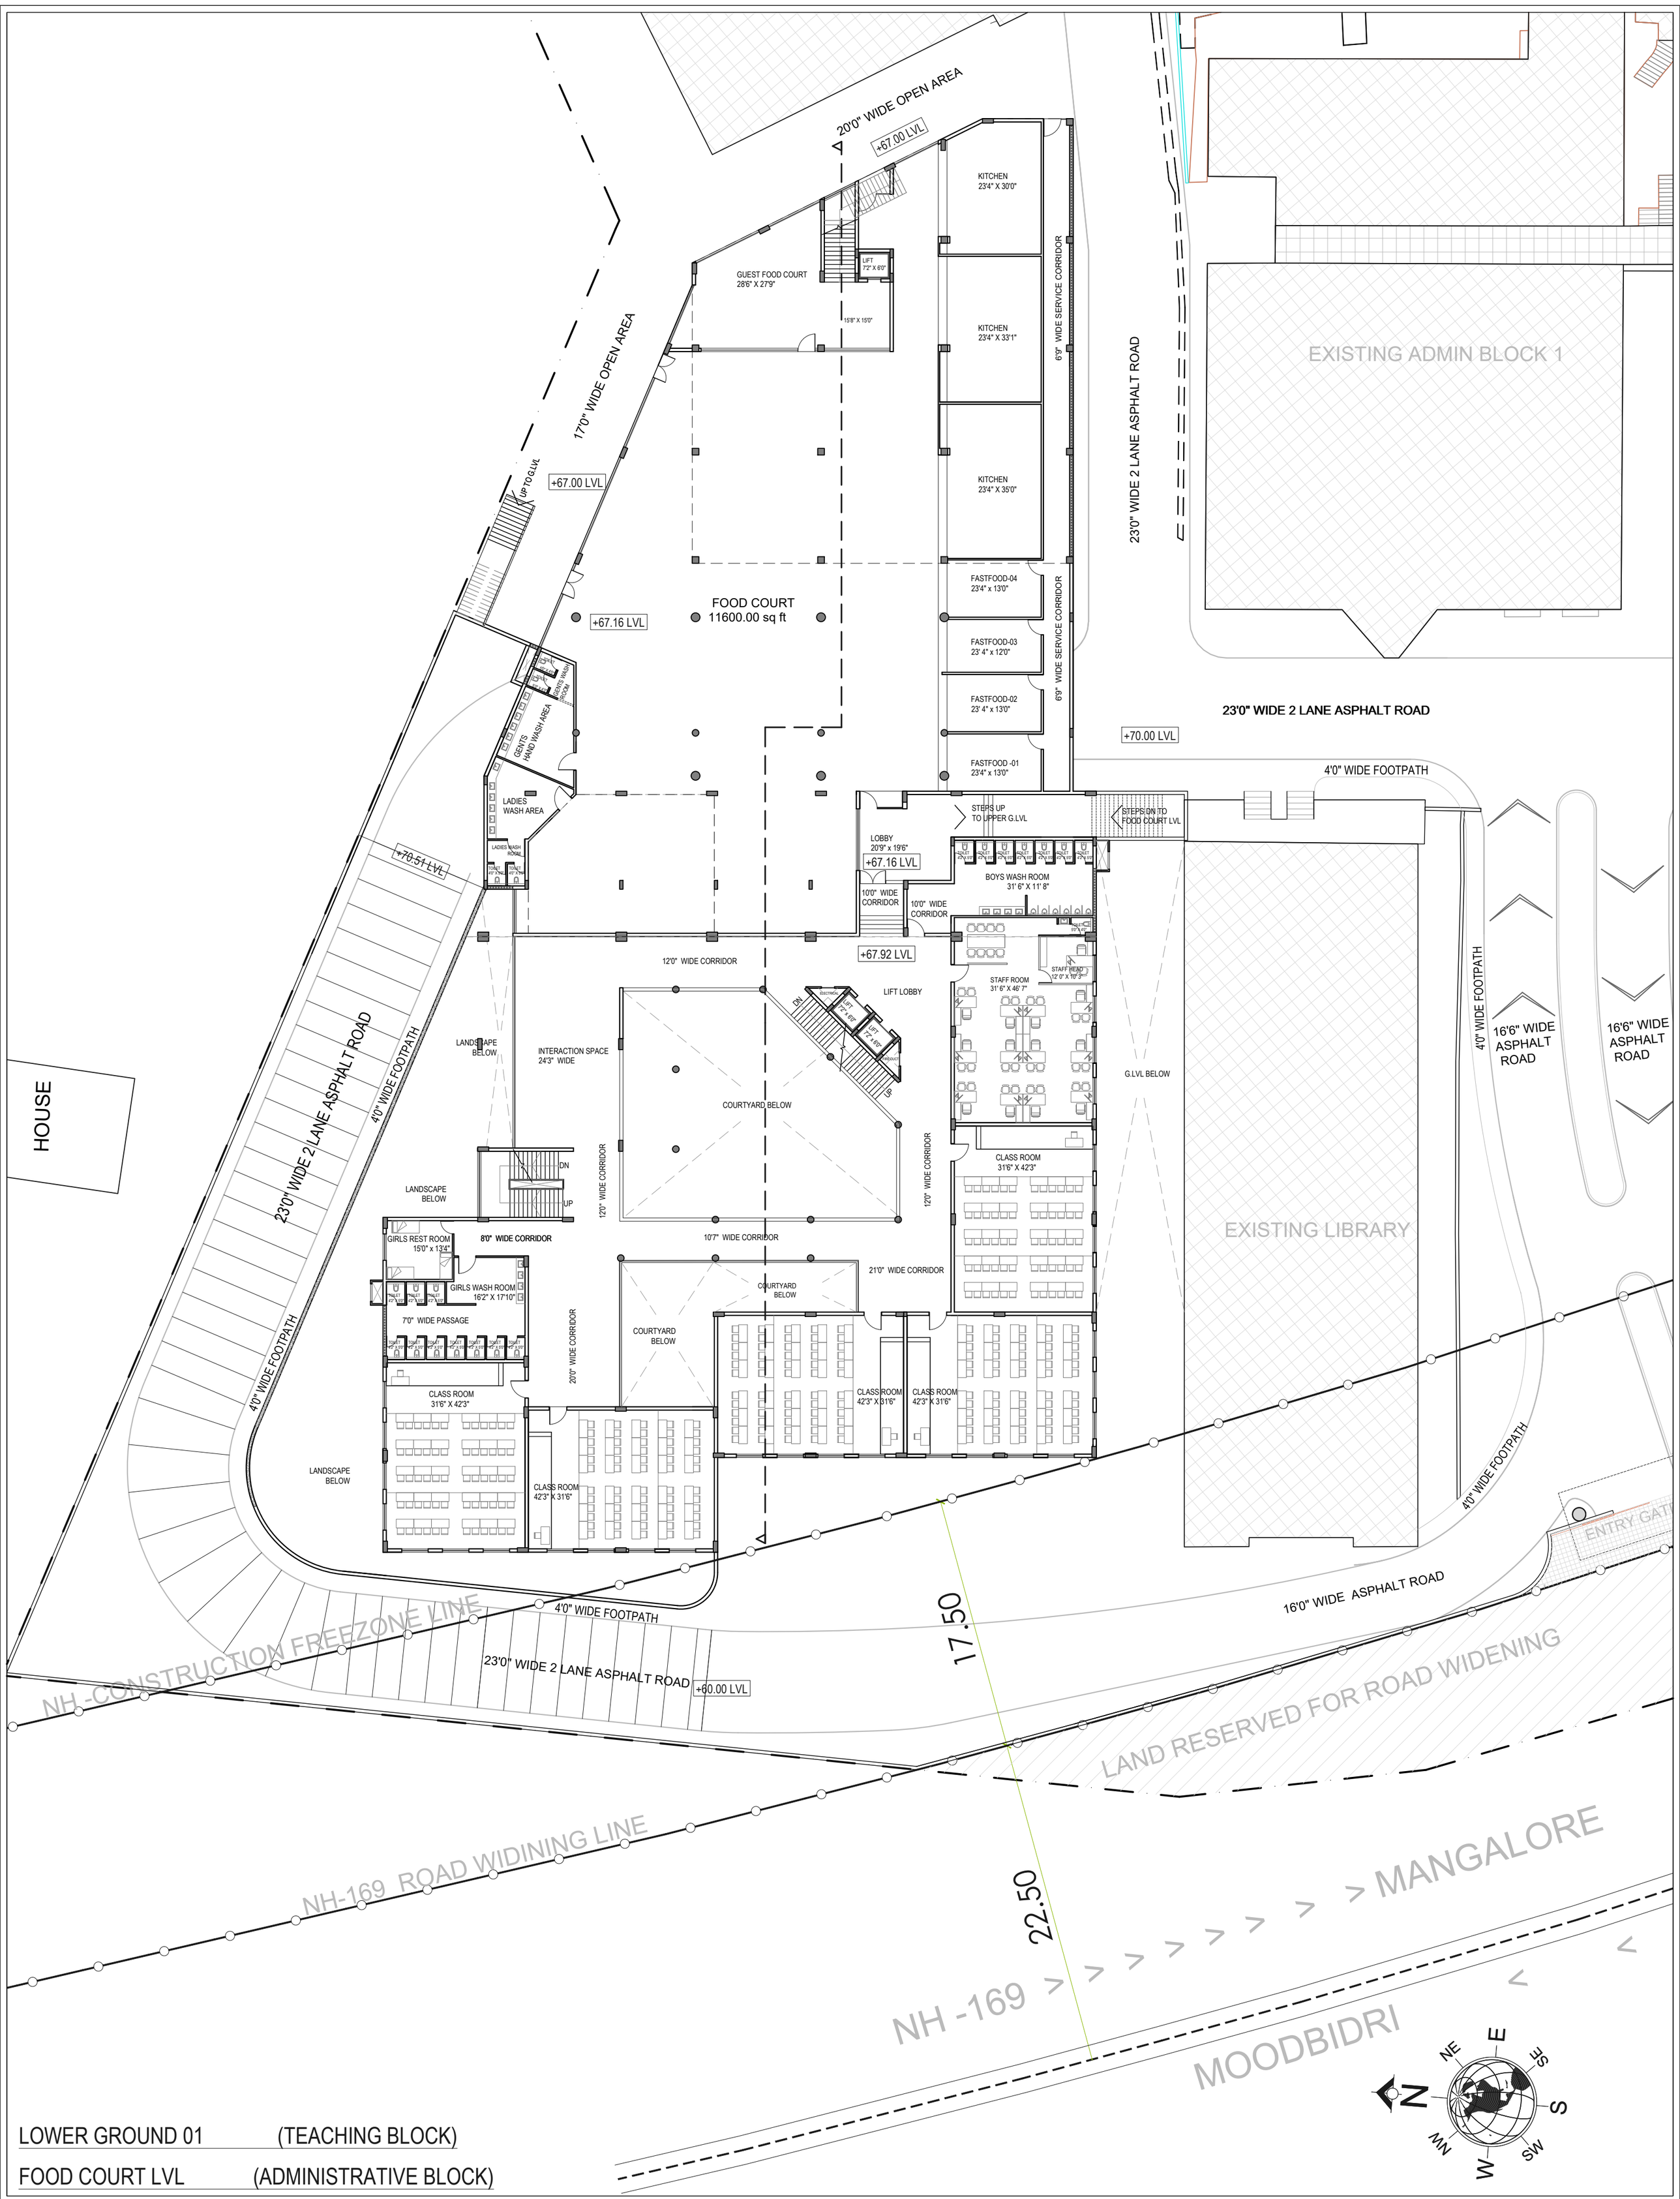

LOWER GROUND 01 (TEACHING BLOCK)

FOOD COURT LVL (ADMINISTRATIVE BLOCK)

PROPOSED ADDITION OF 'ADMINISTRATIVE BLOCK' , TEACHING BLOCK @ AIET CAMPUS MOODBIDRI

SHEET NO- 03 OF 08

2025-INS -58-CS-IP-DRA-ZO-001 V3 R2

DATE: 17/03/2025


SCALE: 1:200

DRAWN BY : J.K

APPROVED BY:S.A

Arch Vista ARCHITECTURE

City Gate Commercial Complex,
4 Floor, Kadri, Mangalore - 575 002
Telephone : (0824 - 2214078)
e - mail : ar.sharun@gmail.com

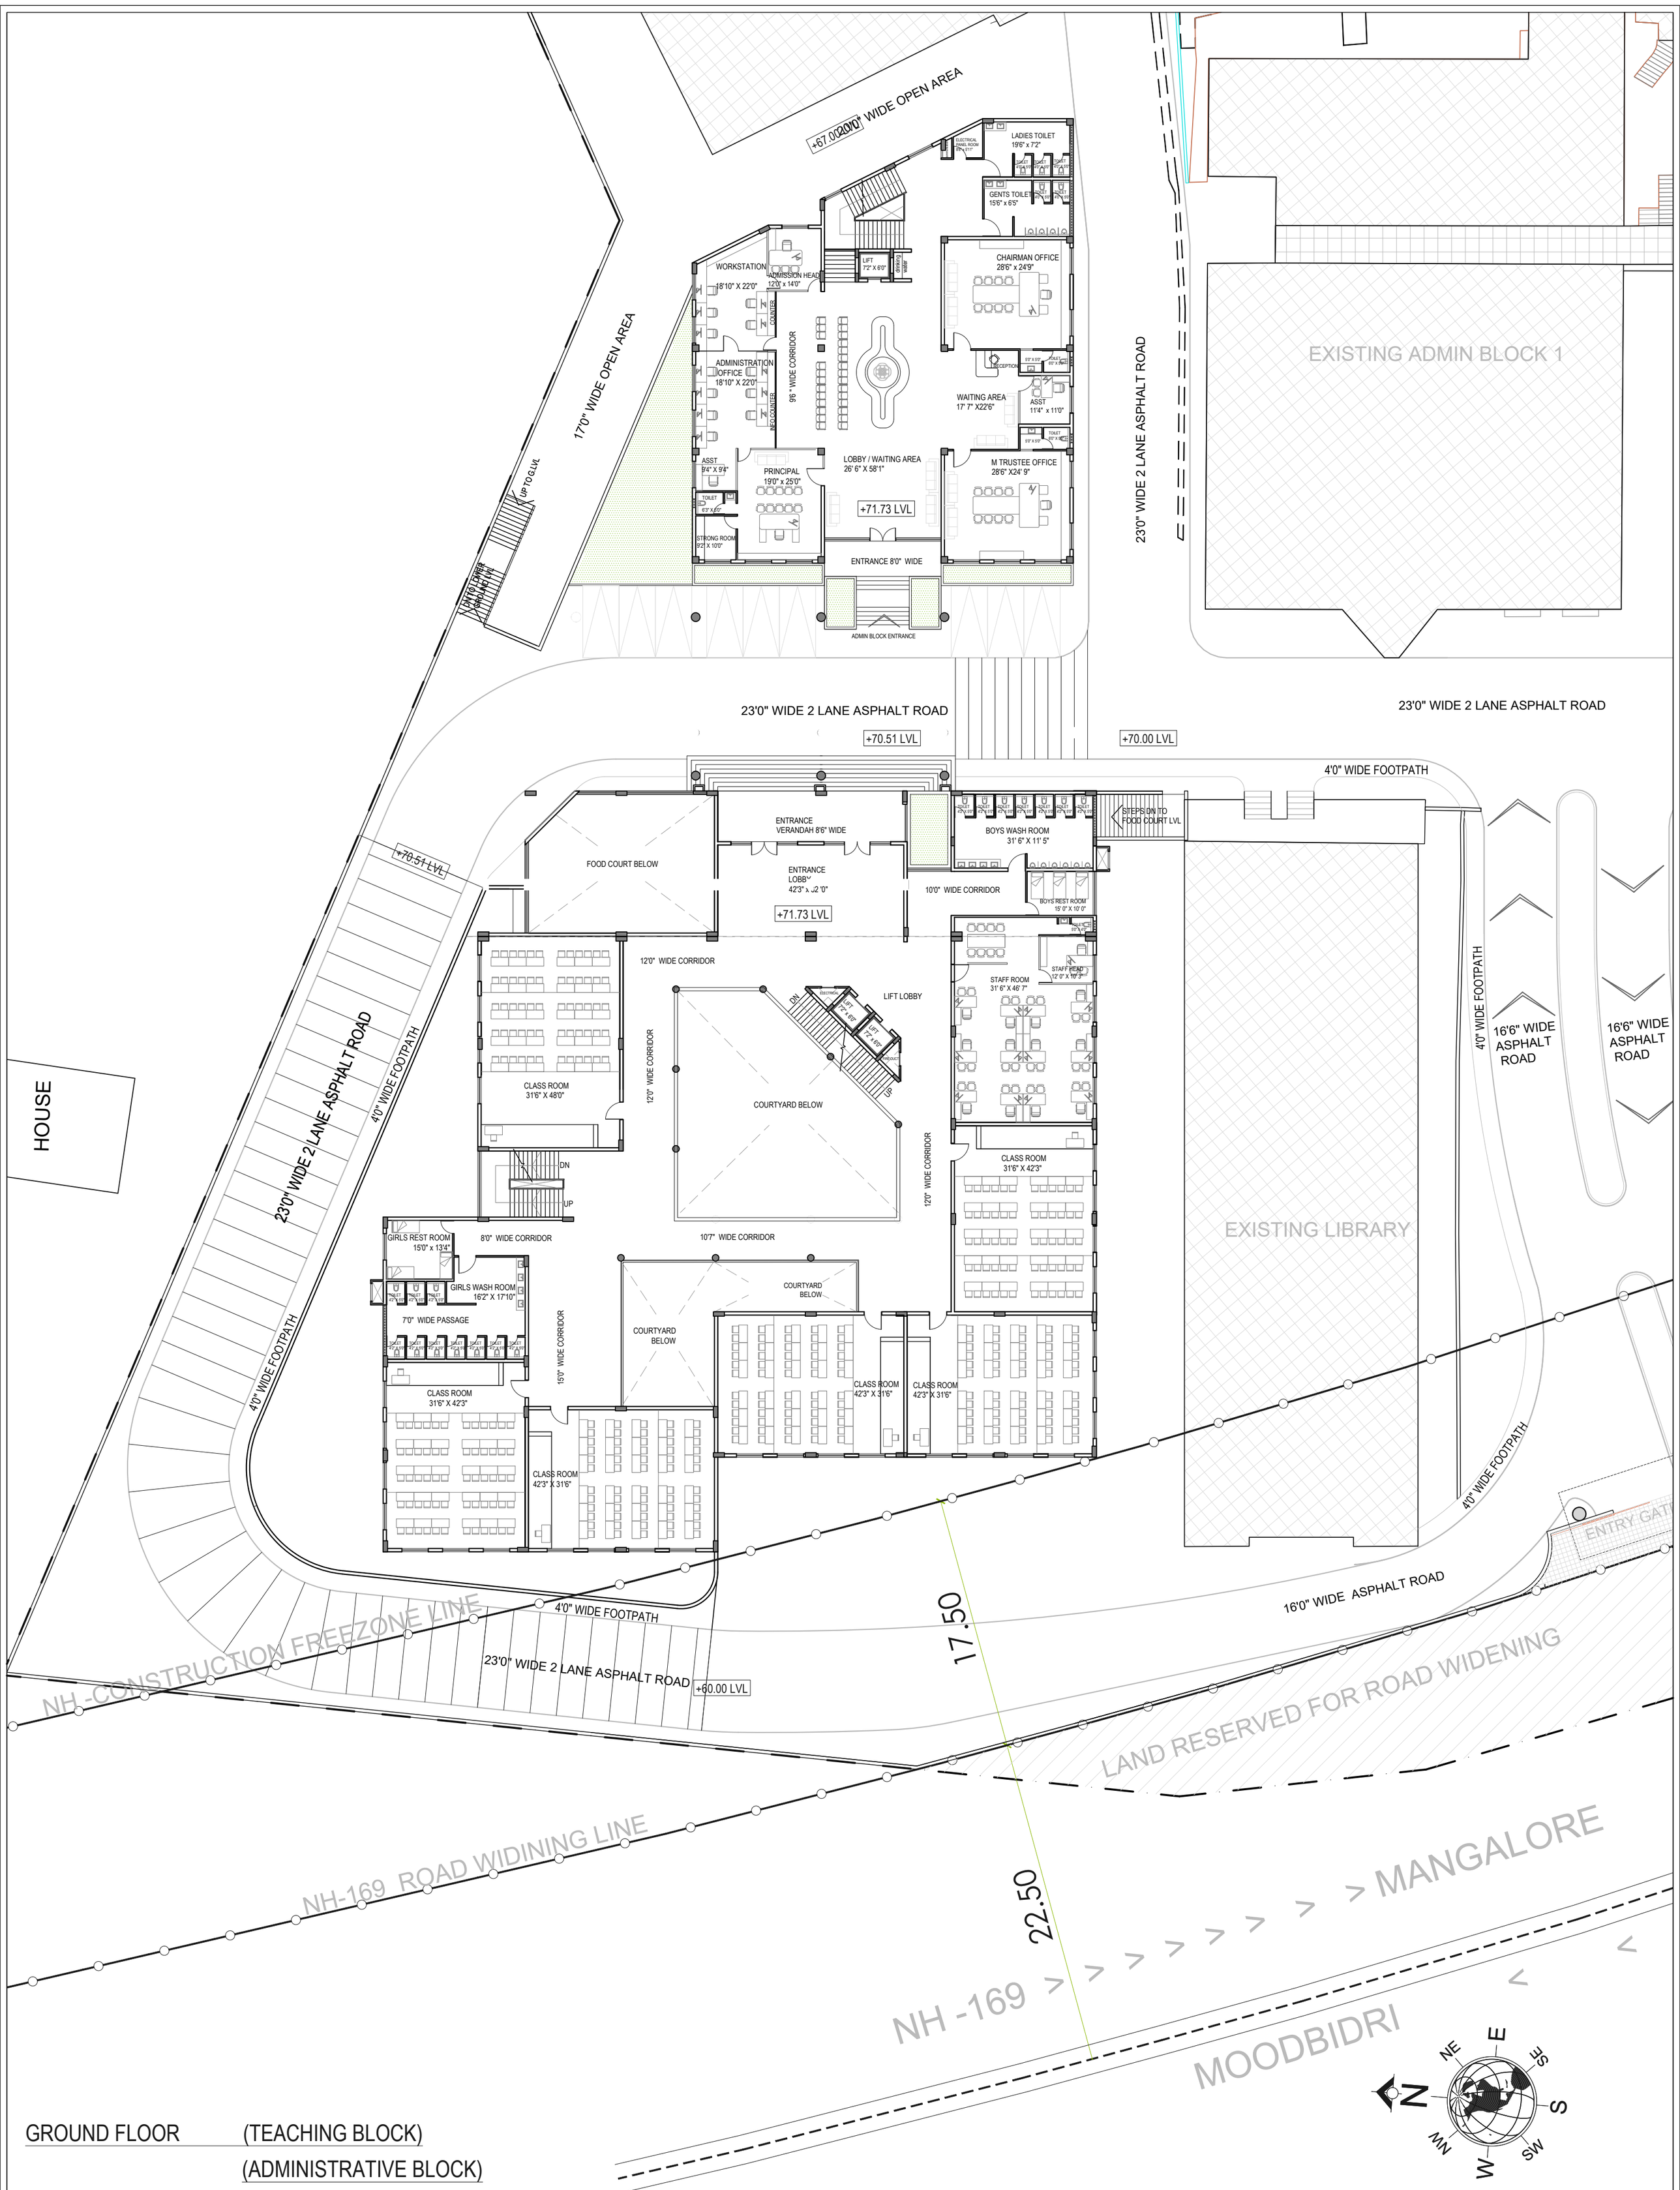

GROUND FLOOR (TEACHING BLOCK)

(ADMINISTRATIVE BLOCK)

PROPOSED ADDITION OF 'ADMINISTRATIVE BLOCK' , TEACHING BLOCK @ AIET CAMPUS MOODBIDRI

SHEET NO- 04 OF 08

2025-INS -58-CS-IP-DRA-ZO-001 V3 R2

DATE: 17/03/2025


SCALE: 1:200

DRAWN BY : J.K

APPROVED BY:S.A

Arch Vista ARCHITECTURE

City Gate Commercial Complex,
4 Floor, Kadri, Mangalore - 575 002
Telephone : (0824 - 2214078)
e - mail : ar.sharun@gmail.com

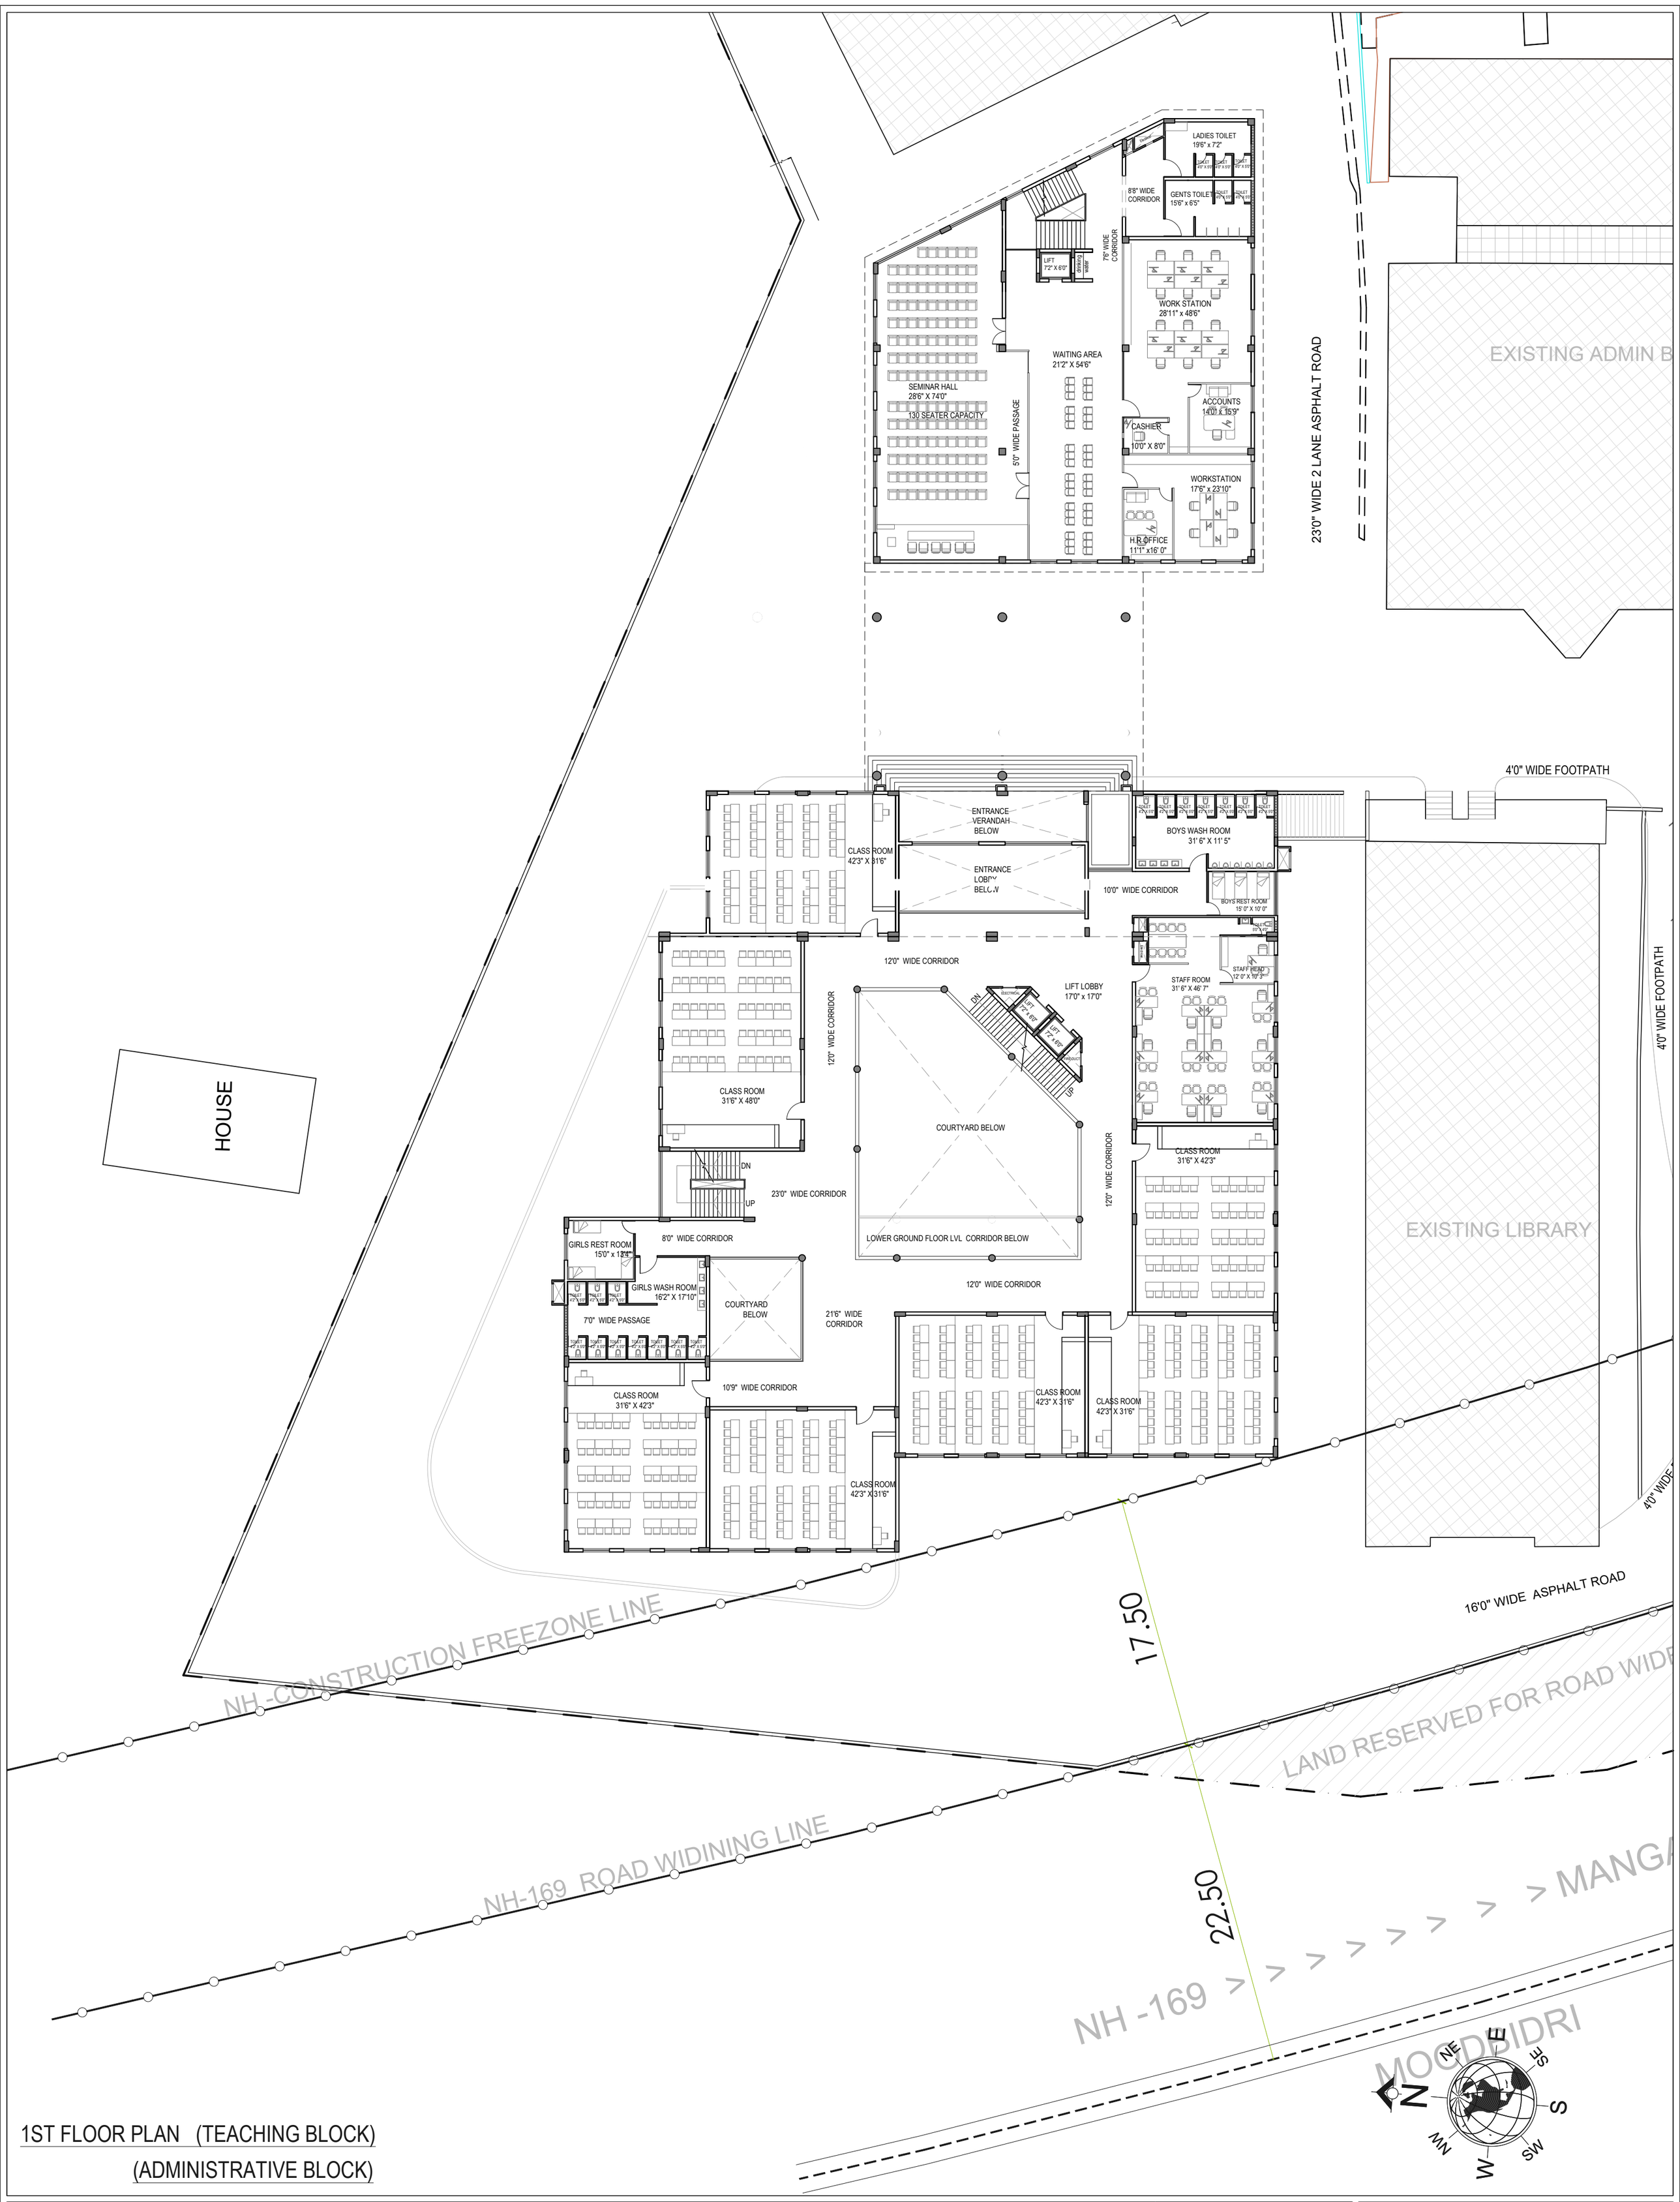

1ST FLOOR PLAN (TEACHING BLOCK)
(ADMINISTRATIVE BLOCK)

PROPOSED ADDITION OF 'ADMINISTRATIVE BLOCK' , TEACHING BLOCK
@ AIET CAMPUS MOODBIDRI

SHEET NO- 05 OF 08

2025-INS -58-CS-IP-DRA-ZO-001 V3 R2


DATE: 17/03/2025

SCALE: 1:200

DRAWN BY : J.K

APPROVED BY:S.A

Arch Vista ARCHITECTURE
City Gate Commercial Complex,
4 Floor, Kadri, Mangalore - 575 002
Telephone : (0824 - 2214078)
e - mail : ar.sharun@gmail.com

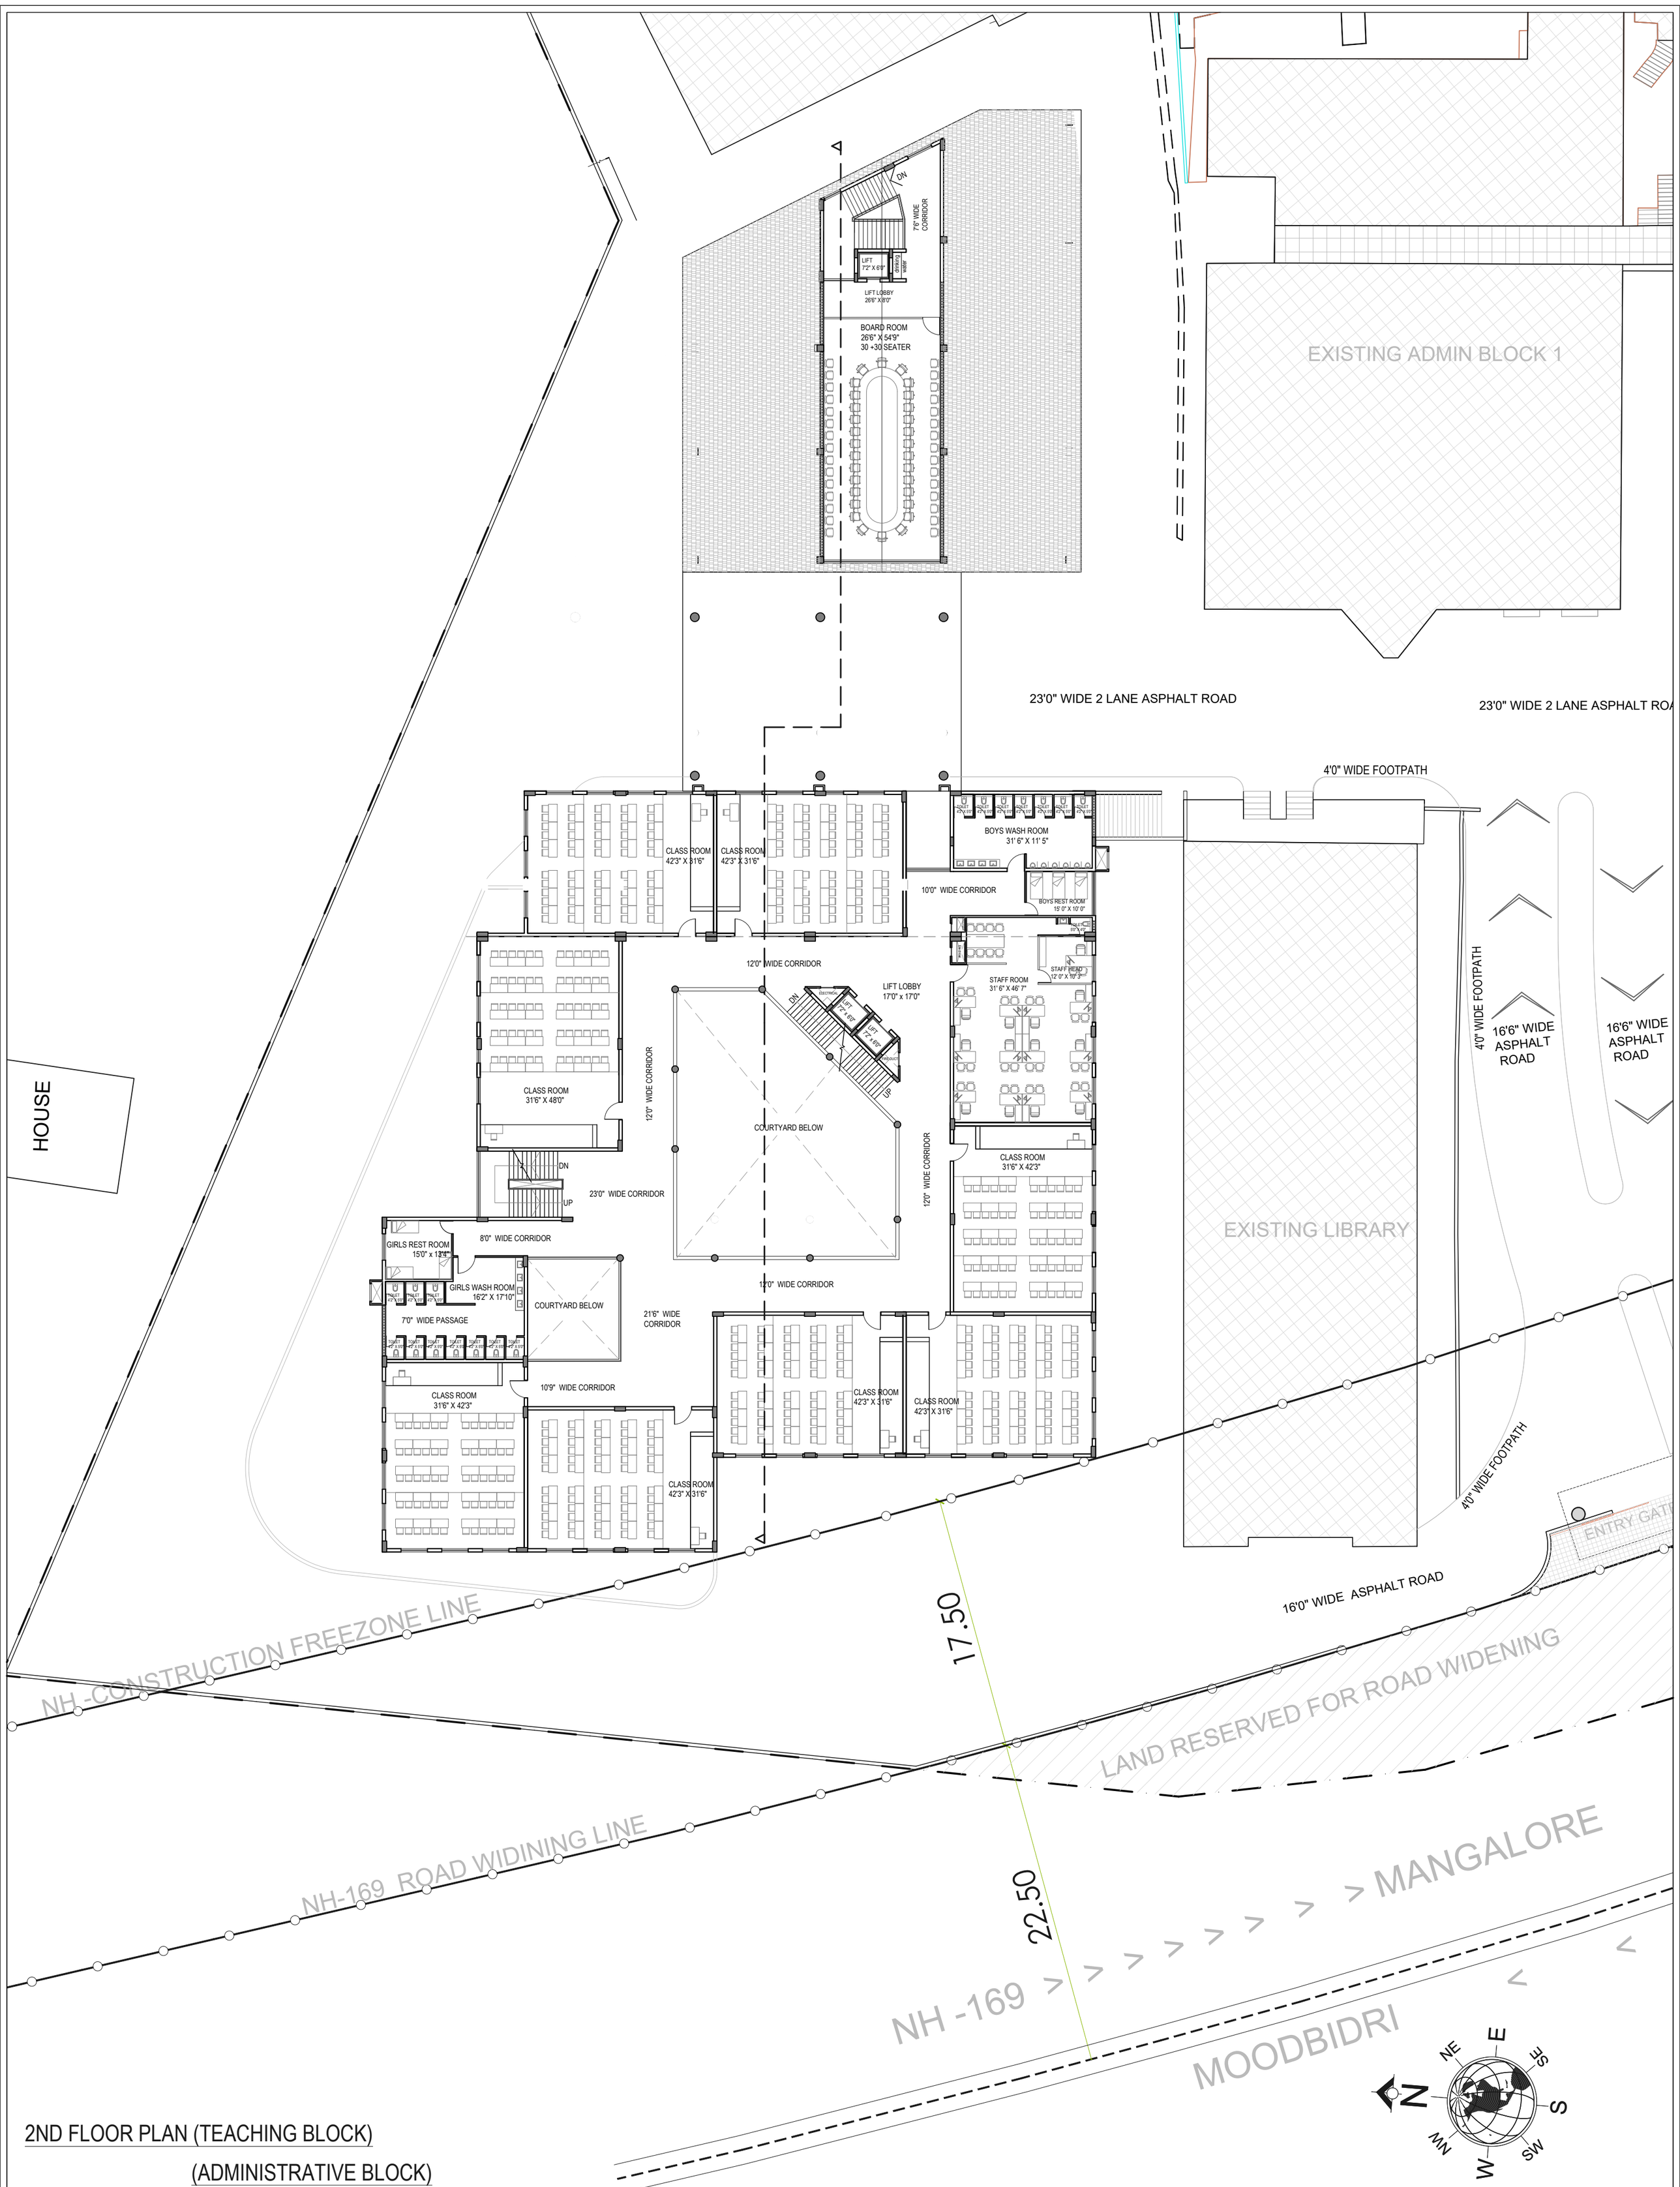

2ND FLOOR PLAN (TEACHING BLOCK)

(ADMINISTRATIVE BLOCK)

PROPOSED ADDITION OF 'ADMINISTRATIVE BLOCK' , TEACHING BLOCK @ AIET CAMPUS MOODBIDRI

SHEET NO- 06 OF 08

2025-INS -58-CS-IP-DRA-ZO-001 V3 R2

DATE: 17/03/2025

SCALE: 1:200

DRAWN BY : J.K

APPROVED BY:S.A

Arch Vista ARCHITECTURE

City Gate Commercial Complex,
4 Floor, Kadri, Mangalore - 575 002
Telephone : (0824 - 2214078)
e - mail : ar.sharun@gmail.com